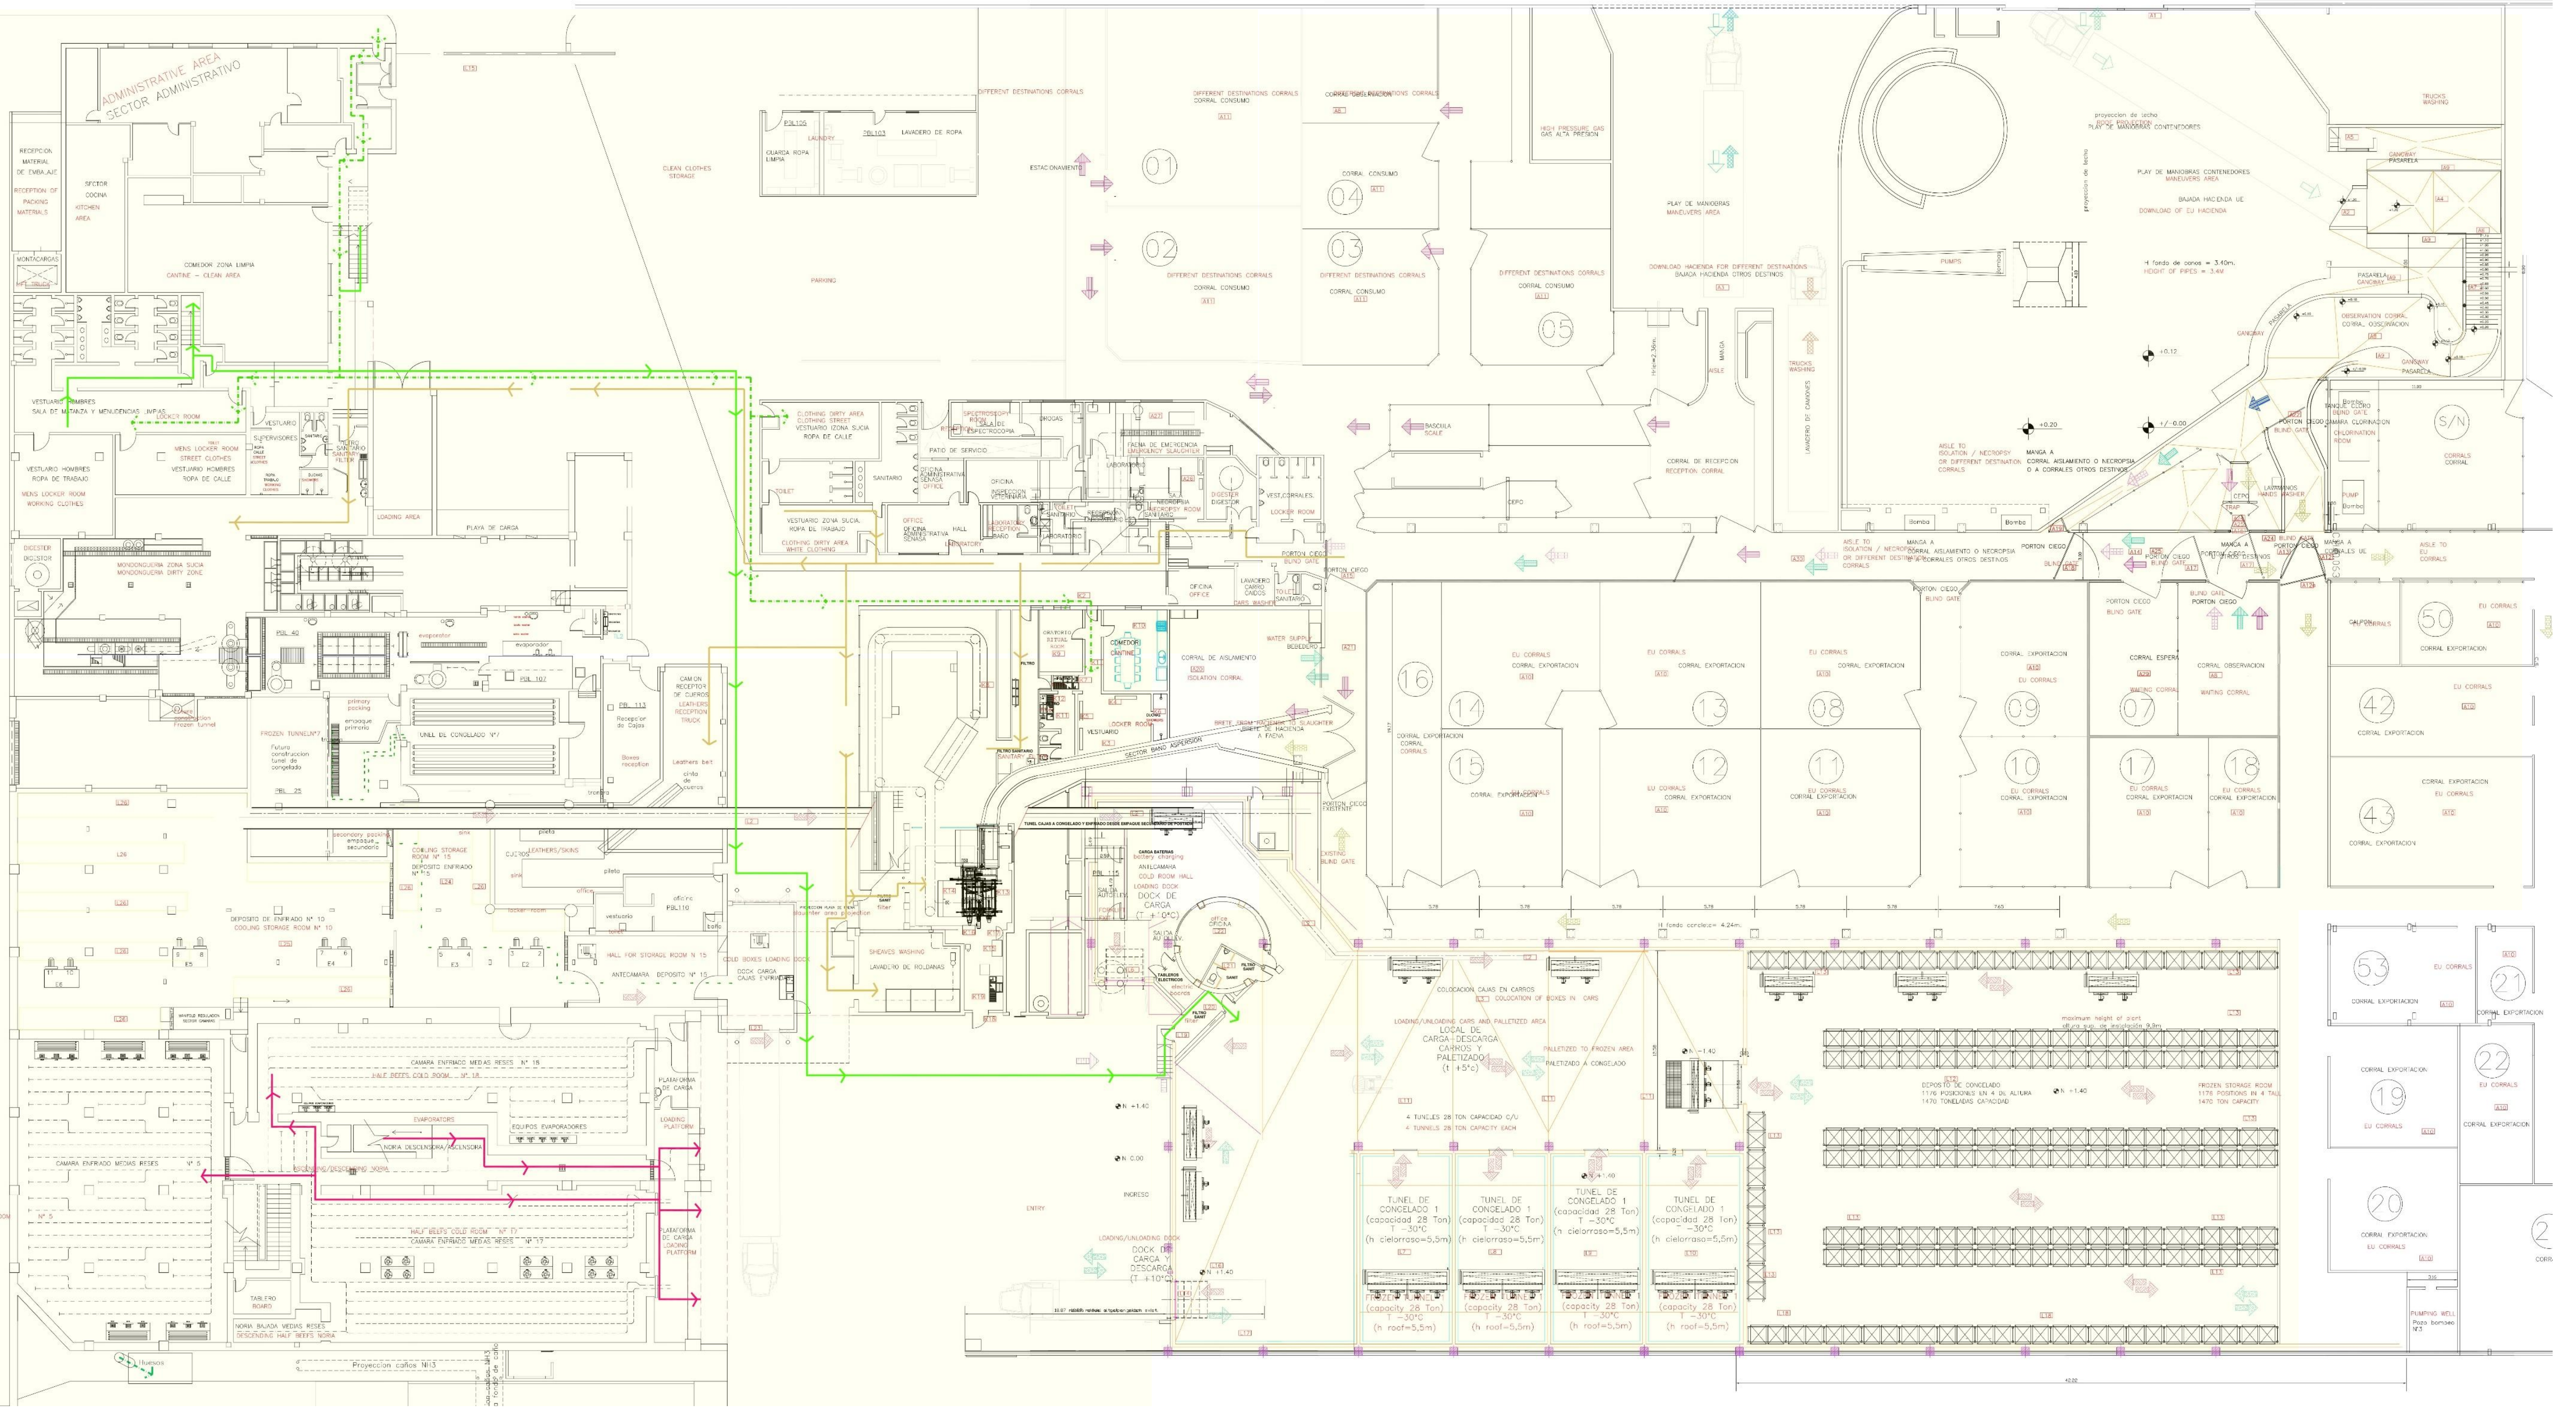
ADMINISTRATIVE AREA
SECTOR ADMINISTRATIVO
RECEPCION MATERIAL DE EMBALAJE
RECEPTION OF PACKING MATERIALS
SECTOR COCINA
KITCHEN AREA
MONTACARGAS
COMEDOR ZONA LIMPIA
CANTINE - CLEAN AREA
VESTUARIO HOMBRES SALA DE MATANZA Y MENUDENCIAS LIMPIAS
LOCKER ROOM
VESTUARIO HOMBRES ROPA DE TRABAJO
MENS LOCKER ROOM WORKING CLOTHES
MENS LOCKER ROOM STREET CLOTHES
VESTUARIO HOMBRES ROPA DE CALLE
VESTUARIO SUPERVISORES
DIGESTER
DIGESTOR
MONDONGUERIA ZONA SUCIA
MONDONGUERIA DIRTY ZONE
LOADING AREA
PLAYA DE CARGA
FROZEN TUNNEL N°7
Futuro construccion tunel de congelado
TUNEL DE CONGELADO N°7
primary packing
empaque primario
evaporator
evaporador
Receptor de Cajas
Boxes reception
CAMION RECEPTOR DE CUEROS
LEATHERS RECEPTION TRUCK
Leathers belt
cinta de cueros
secondary packing
empaque secundario
COOLING STORAGE ROOM N° 15
DEPOSITO ENFRIADO N° 15
LEATHERS/SKINS
DEPOSITO DE ENFRIADO N° 10
COOLING STORAGE ROOM N° 10
HALL FOR STORAGE ROOM N 15
ANTECAMARA DEPOSITO N° 15
COLD BOXES LOADING DOCK
DOCK CARGA CAJAS
CAMARA ENFRIADO MEDIAS RESES N° 18
HALF BEEFS COLD ROOM N° 18
EVAPORATORS
EQUIPOS EVAPORADORES
NORIA DESCENSORA/ASCENSORA
CAMARA ENFRIADO MEDIAS RESES N° 5
HALF BEEFS COLD ROOM N° 17
CAMARA ENFRIADO MEDIAS RESES N° 17
PLATAFORMA DE CARGA
LOADING PLATFORM
TABLERO
BOARD
NORIA BAJADA MEDIAS RESES
DESCENDING HALF BEEFS NORIA
Huesos
Proyeccion caños N°13
CLEAN CLOTHES STORAGE
LAUNDRY
LAVADERO DE ROPA
GUARDA ROPA LIMPIA
PARKING
ESTACIONAMIENTO
CLOTHING DIRTY AREA
CLOTHING STREET
VESTUARIO ZONA SUCIA ROPA DE CALLE
PATIO DE SERVICIO
SANITARIO
OFICINA ADMINISTRATIVA SENASA
OFICINA INSPECCION VETERINARIA
LABORATORIO
FAENA DE EMERGENCIA
EMERGENCY SLAUGHTER
NECROPSIA
NECROPSY ROOM
DIGESTER
DIGESTOR
VESTUARIO CORRALES
LOCKER ROOM
OFICINA
OFFICE
LAVADERO CARROS CONDOS
CARS WASHER
PORTON CIEGO
BLIND GATE
COMEDOR
CANTINE
LOCKER ROOM
VESTUARIO
CORRAL DE AISLAMIENTO
ISOLATION CORRAL
WATER SUPPLY
BEBEDERO
BRETE FROM ... TO SLAUGHTER
BRETE DE HACIENDA A FAENA
SECTOR BAÑO ASPERSION
CARGA BATERIAS
battery charging
ANTECAMARA
COLD ROOM HALL
LOADING DOCK
DOCK DE CARGA
OFICINA
office
SHEAVES WASHING
LAVADERO DE ROLDANAS
ENTRY
INGRESO
LOADING/UNLOADING DOCK
DOCK DE CARGA Y DESCARGA (T +10°C)
DIFFERENT DESTINATIONS CORRALS
CORRAL CONSUMO
01
02
03
04
05
HIGH PRESSURE GAS
GAS ALTA PRESION
PLAY DE MANIOBRAS
MANEUVERS AREA
DOWNLOAD HACIENDA FOR DIFFERENT DESTINATIONS
BAJADA HACIENDA OTROS DESTINOS
TRUCKS WASHING
LAVADERO DE CAMIONES
MANGA
AISLE
BASCULA
SCALE
CORRAL DE RECEPCION
RECEPTION CORRAL
proyeccion de techo
ROOF PROJECTION
PLAY DE MANIOBRAS CONTENEDORES
MANEUVERS AREA
BAJADA HACIENDA UE
DOWNLOAD OF EU HACIENDA
PUMPS
H fondo de conos = 3.40m.
HEIGHT OF PIPES = 3.4M
PASARELA
GANGWAY
OBSERVATION CORRAL
CORRAL OBSERVACION
TRUCKS WASHING
AISLE TO ISOLATION / NECROPSY OR DIFFERENT DESTINATION CORRALS
MANGA A CORRAL AISLAMIENTO O NECROPSIA O A CORRALES OTROS DESTINOS
TANQUE CLORO
CHLORINATION ROOM
LAVAMANOS
HANDS WASHER
S/N
CORRALES
NORMAL
Bombe
PUMP
AISLE TO EU CORRALS
MANGA A CORRALES UE
EU CORRALS
CORRAL EXPORTACION
16
14
13
08
09
07
15
12
11
10
17
18
50
42
43
CORRAL ESPERA
WAITING CORRAL
CORRAL OBSERVACION
EXISTING BLIND GATE
H fondo concreto= 4.24m.
COLOCACION CAJAS EN CARROS
COLOCATION OF BOXES IN CARS
LOADING/UNLOADING CARS AND PALLETIZED AREA
LOCAL DE CARGA-DESCARGA CARROS Y PALETIZADO (t +5°c)
PALLETIZED TO FROZEN AREA
PALETIZADO A CONGELADO
4 TUNELES 28 TON CAPACIDAD C/U
4 TUNNELS 28 TON CAPACITY EACH
TUNEL DE CONGELADO 1 (capacidad 28 Ton) T -30°C (h cielorraso=5,5m)
FROZEN TUNNEL (capacity 28 Ton) T -30°C (h roof=5,5m)
maximum height of plant
DEPOSITO DE CONGELADO
1176 POSICIONES EN 4 DE ALTURA
1470 TONELADAS CAPACIDAD
FROZEN STORAGE ROOM
1176 POSITIONS IN 4 TALL
1470 TON CAPACITY
53
21
22
19
20
PUMPING WELL
Pozo bombeo N°3